
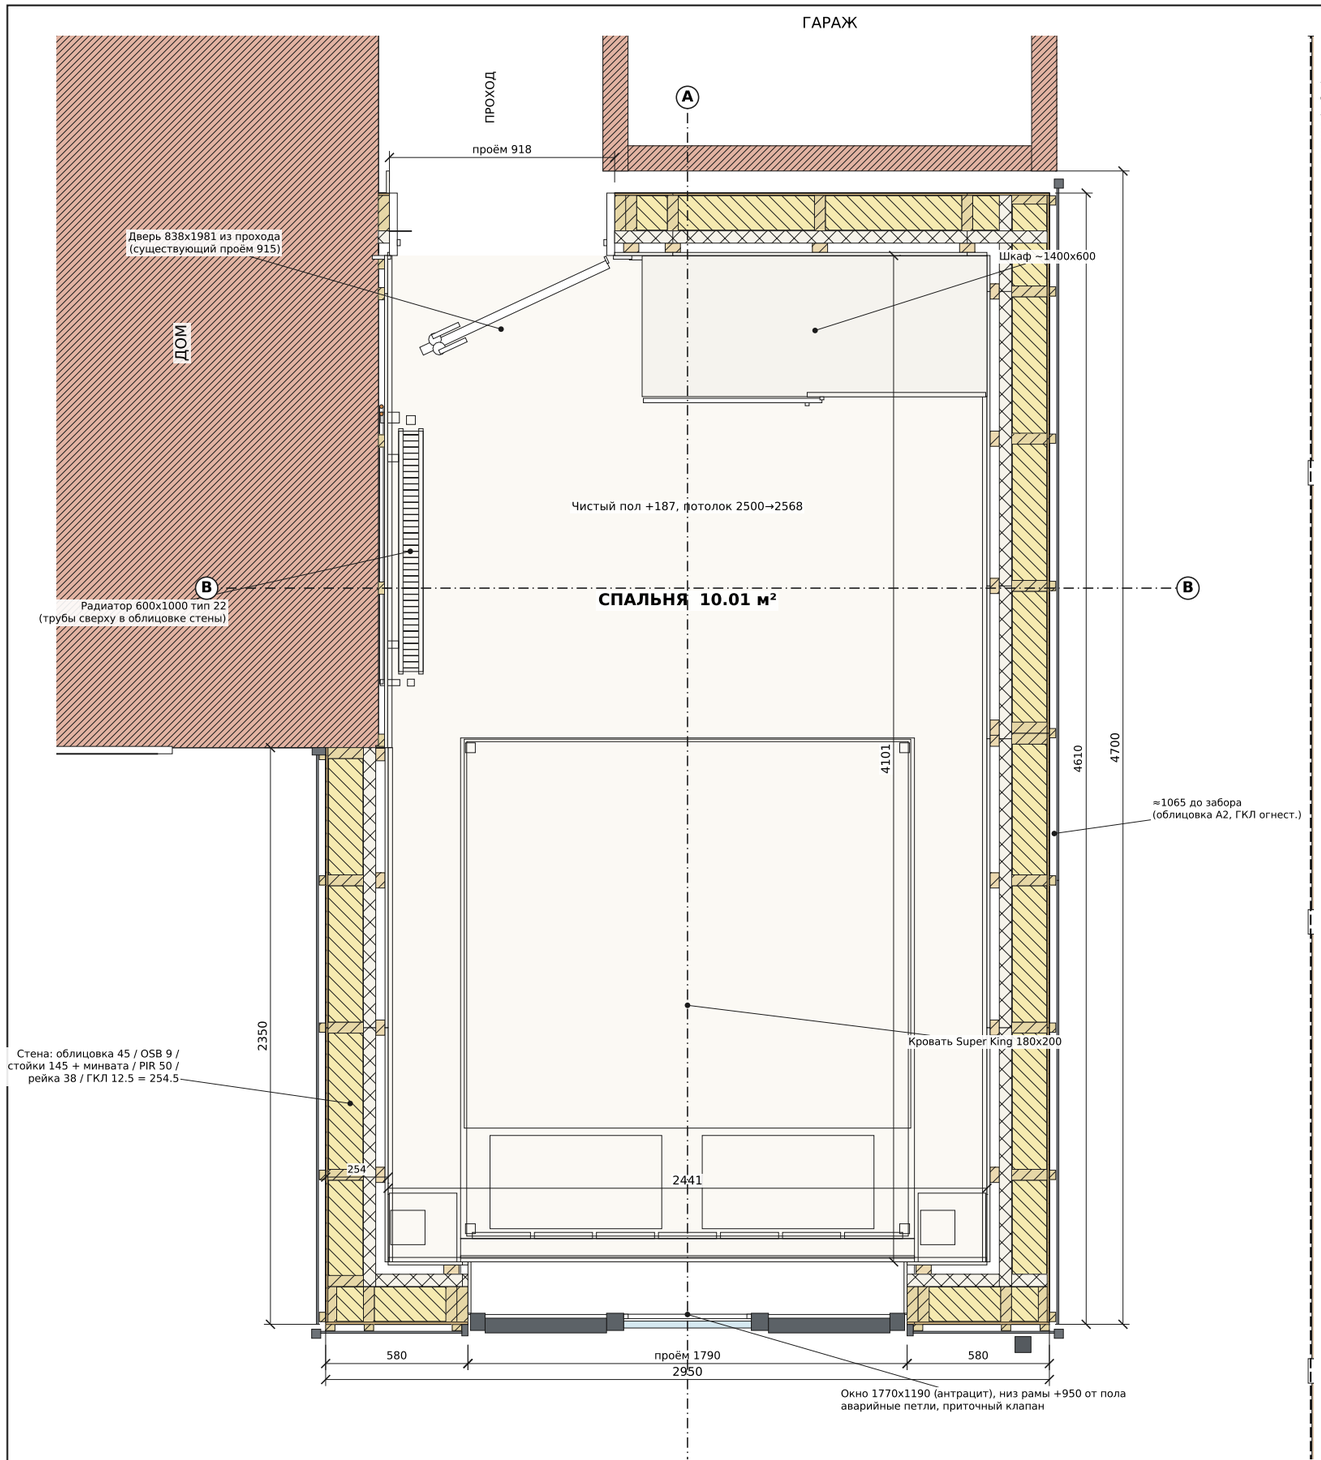


ПЛАН ПОМЕЩЕНИЯ (разрез на +1200)

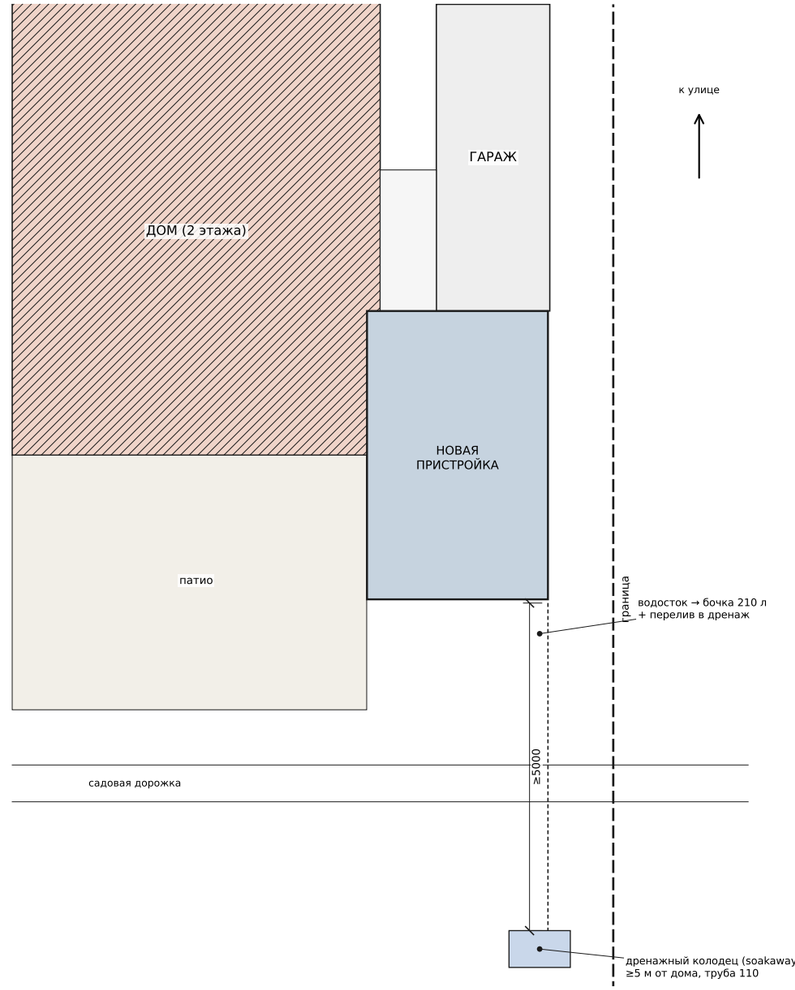


СИТУАЦИОННЫЙ ПЛАН 1:100


ПРИМЕЧАНИЯ

1. Отметка 0.000 = верх существующего фундамента (2 ряда блоков). Земля −195.
2. Чистый пол +187 (проход +195): переход порожком 8–10 мм.
3. Фундамент существующий — глубину подтвердить шурфом для Building Control.
4. Диагонали фундамента 5150/5130: каркас выставить по ровным диагоналям.
5. Расстояние до забора принято ≈1.0 м — уточнить по месту.
6. Электрика: черновая разводка своими силами, подключение и сертификат — электрик с регистрацией Part P.

Пристройка-спальня (каркасная), 2.95 x 4.70 м	
Планы: план этажа (1:25), ситуационный план (1:100)	**Лист 01**
Масштаб 1:25 / 1:100 (A3). Размеры в мм.	10.10.2026 rev A

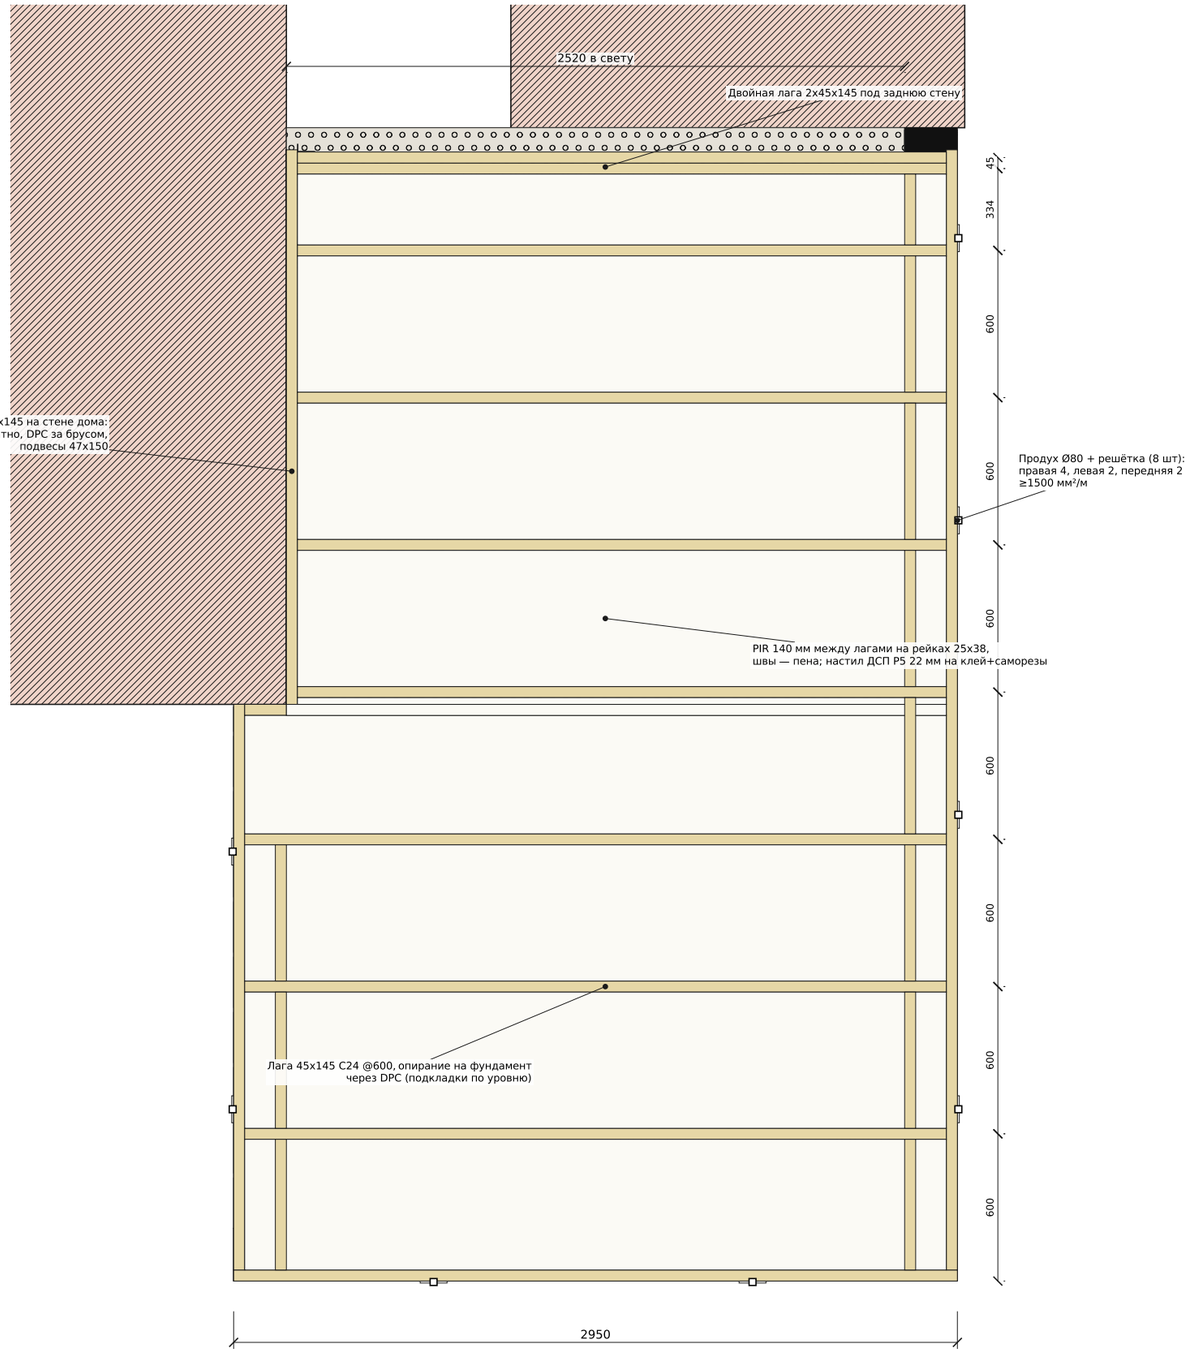


ПЛАН КАРКАСА ПОЛА (вид сверху без настила)

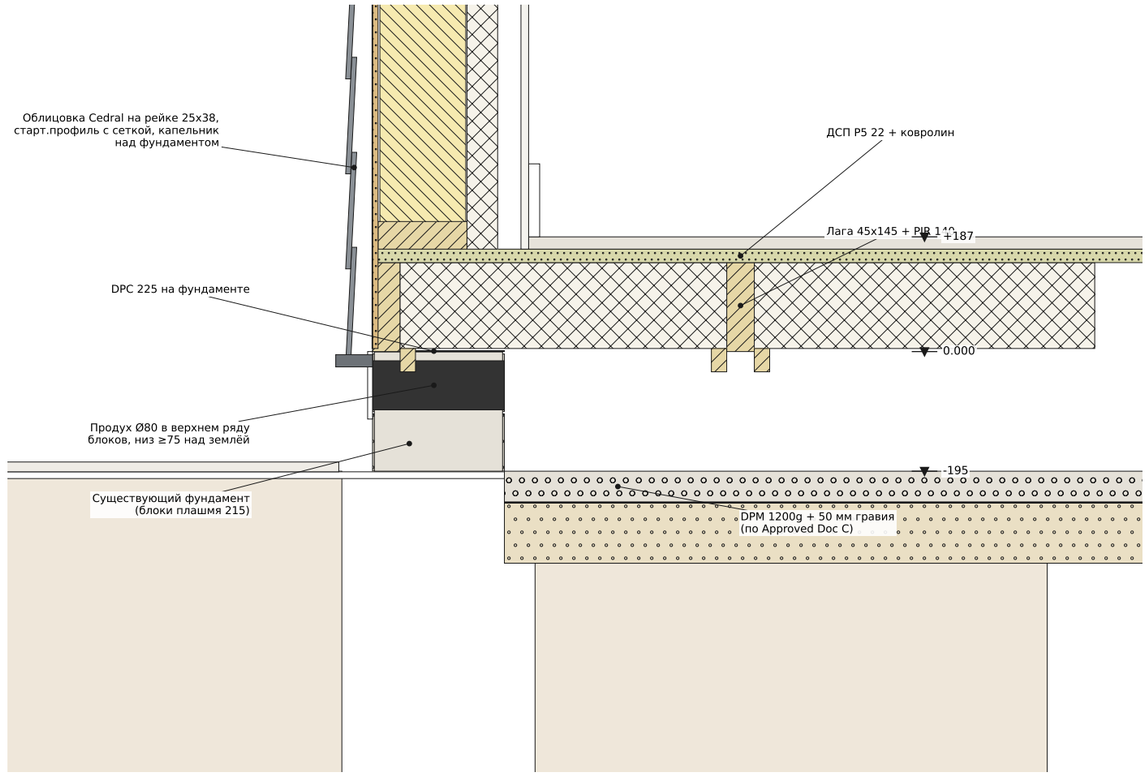


УЗЕЛ 1: цоколь / пол / продух (1:10)

Последовательность: снять дёрн и 150 мм грунта → MOT Type 1 75 + песок 25 → DPM → 50 мм гравия (верх не ниже уровня земли снаружи) → продухи → DPC → лаги → PIR → ДСП. Пространство под полом ≥150 мм (факт ~195). Вентиляция: продухи в двух противоположных стенах ≥1500 мм² на 1 м стены или 500 мм² на 1 м² пола (большее).

Пристройка-спальня (каркасная), 2.95 x 4.70 м	
Фундамент, подполье и каркас пола	**Лист 02**
Масштаб 1:25 / 1:10 (A3)	10.10.2026 rev A

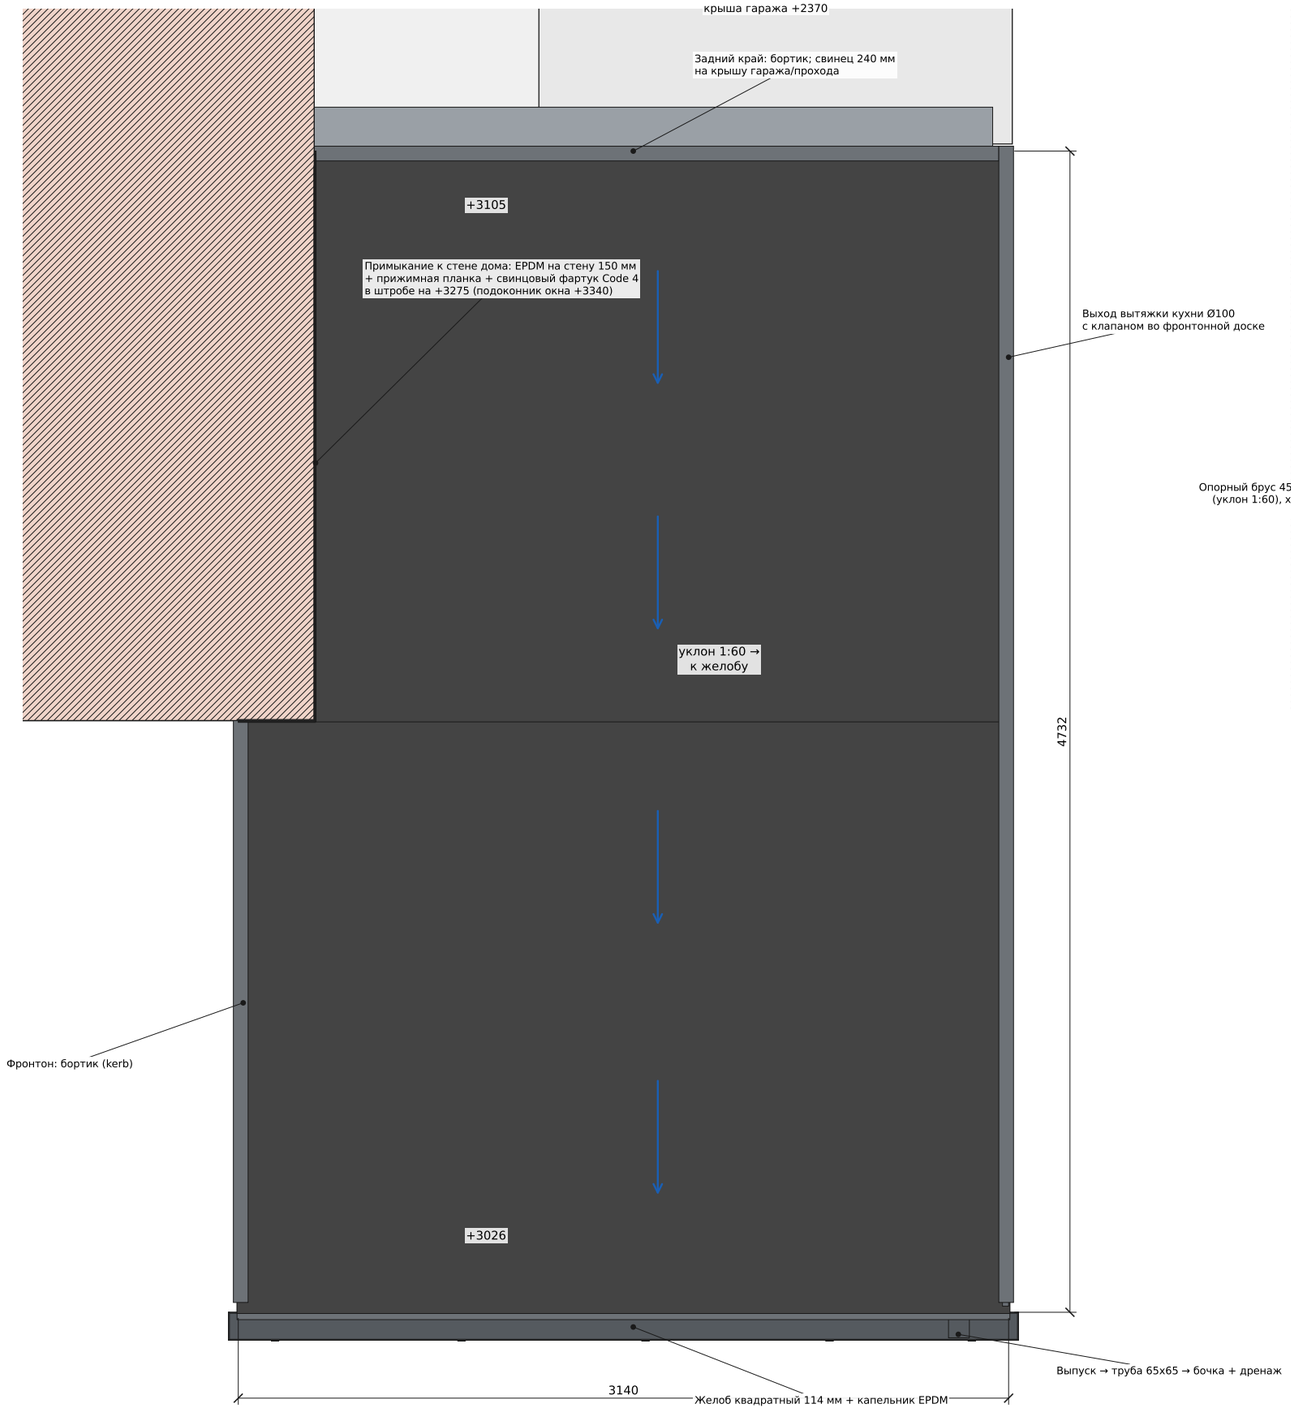


ПЛАН КРОВЛИ (EPDM, уклон 1:60 к окну)

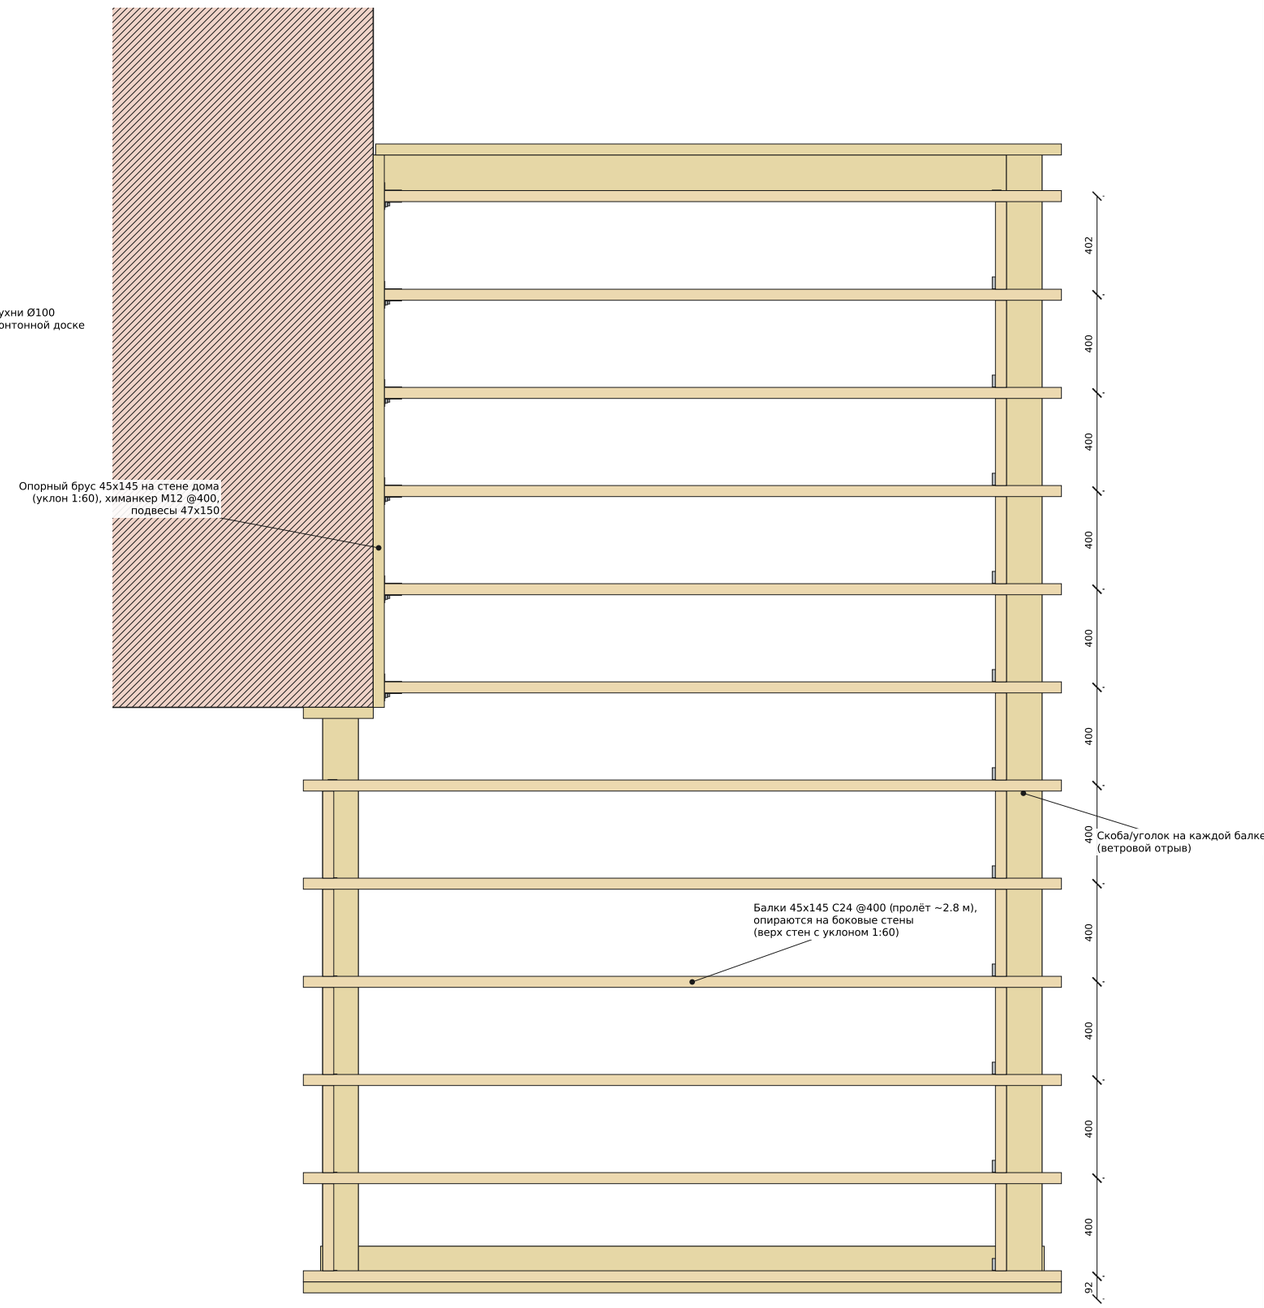


Каждая балка горизонтальна; уклон кровли создаётся разной высотой балок (по наклонной обвязке стен).

РАСКЛАДКА БАЛОК КРОВЛИ


Пристройка-спальня (каркасная), 2.95 x 4.70 м	
Кровля: план кровли и раскладка балок	**Лист 03**
Масштаб 1:25 (A3)	10.10.2026 rev A

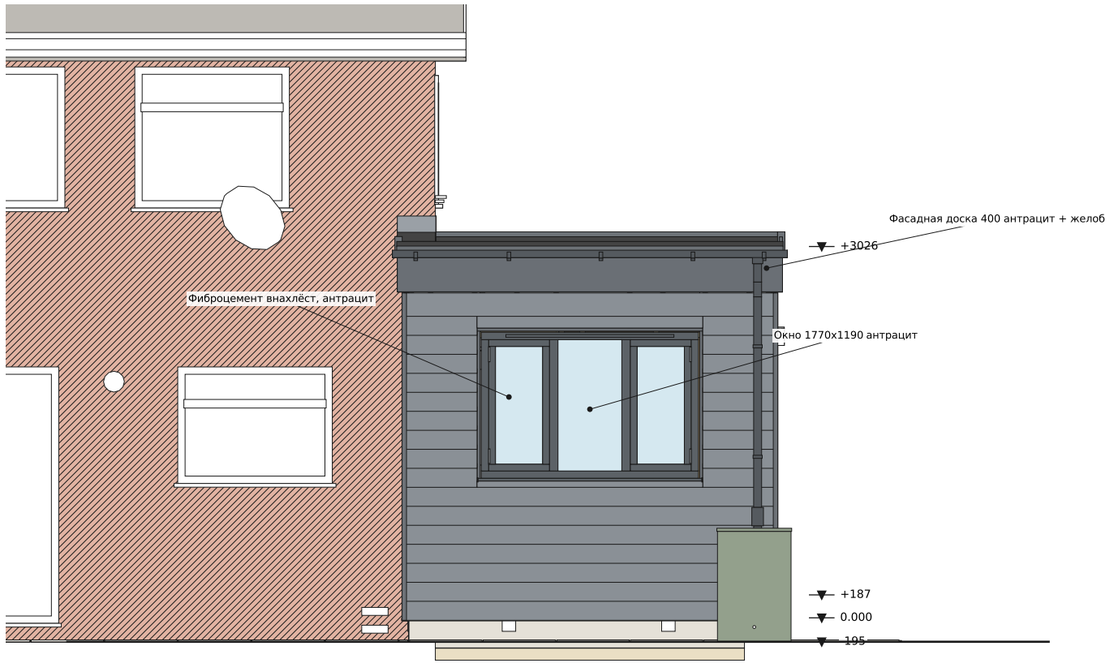


ФАСАД СО СТОРОНЫ САДА

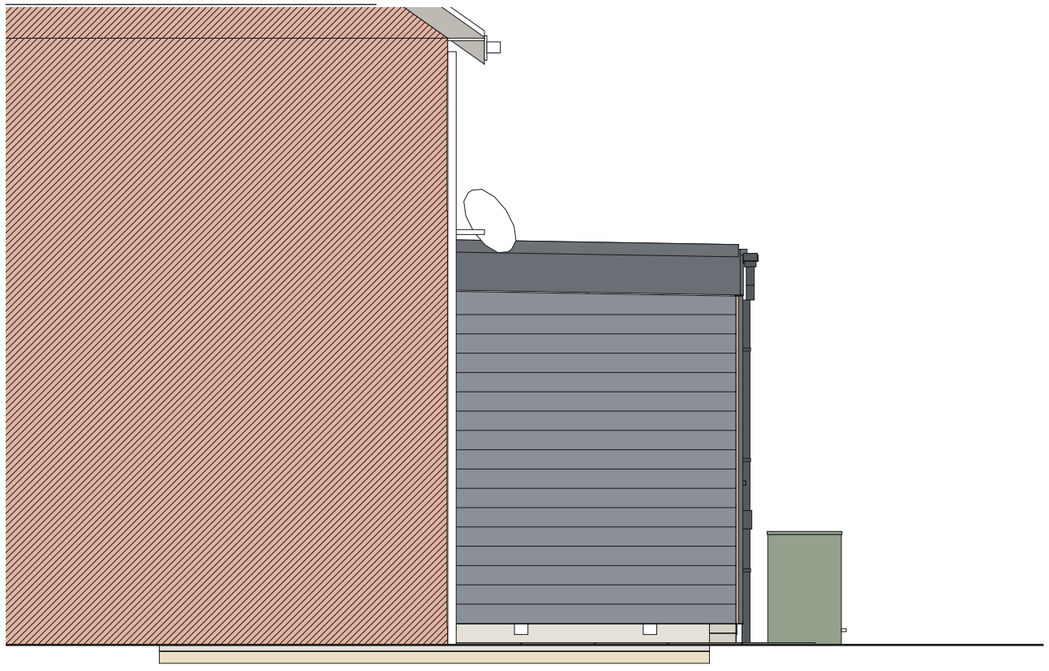

ЛЕВЫЙ ФАСАД (со стороны патио)

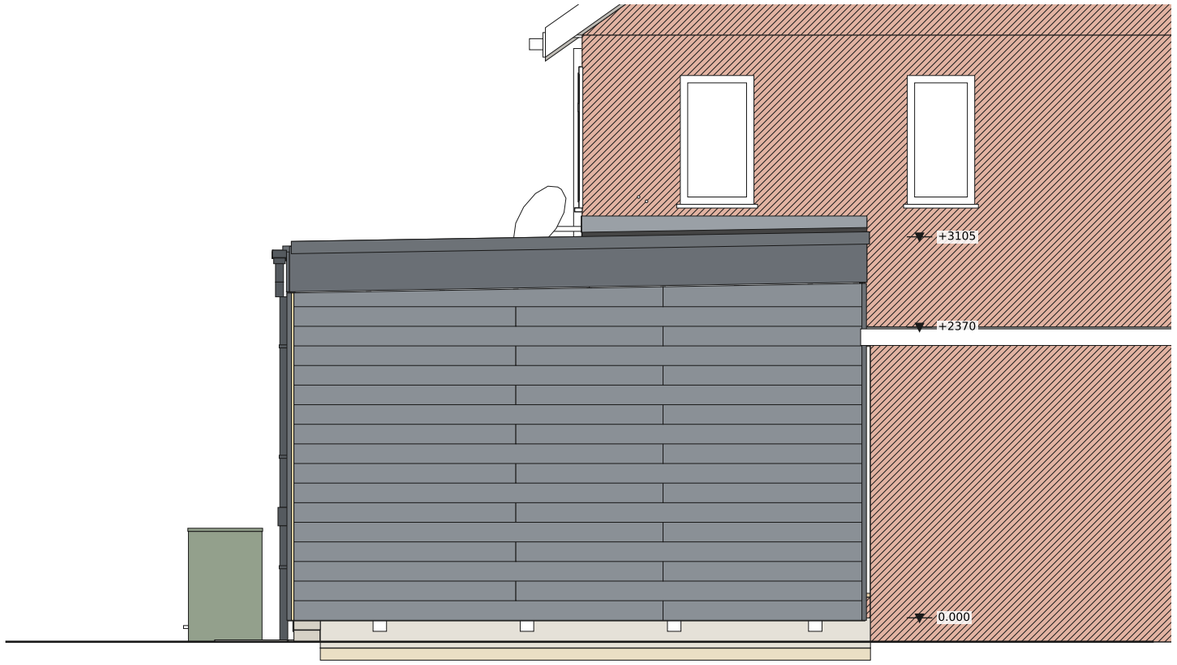


ПРАВЫЙ ФАСАД (со стороны прохода)

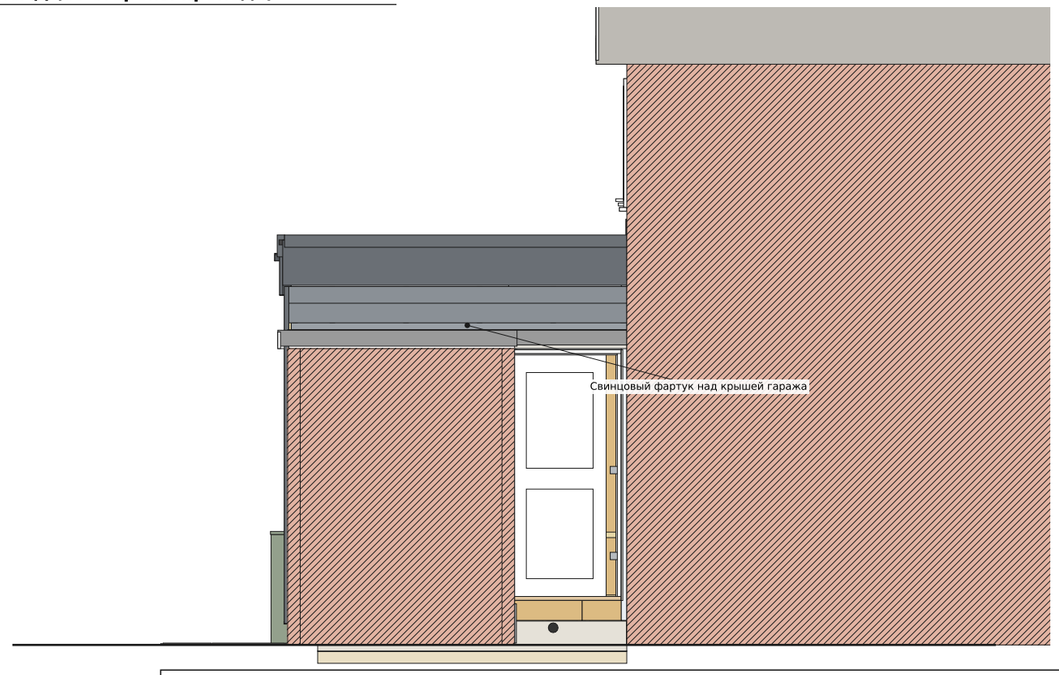

ВИД СЗАДИ (над гаражом)


Пристройка-спальня (каркасная), 2.95 x 4.70 м

Фасады	**Лист 04**
Масштаб 1:50 (A3)	10.10.2026 rev A

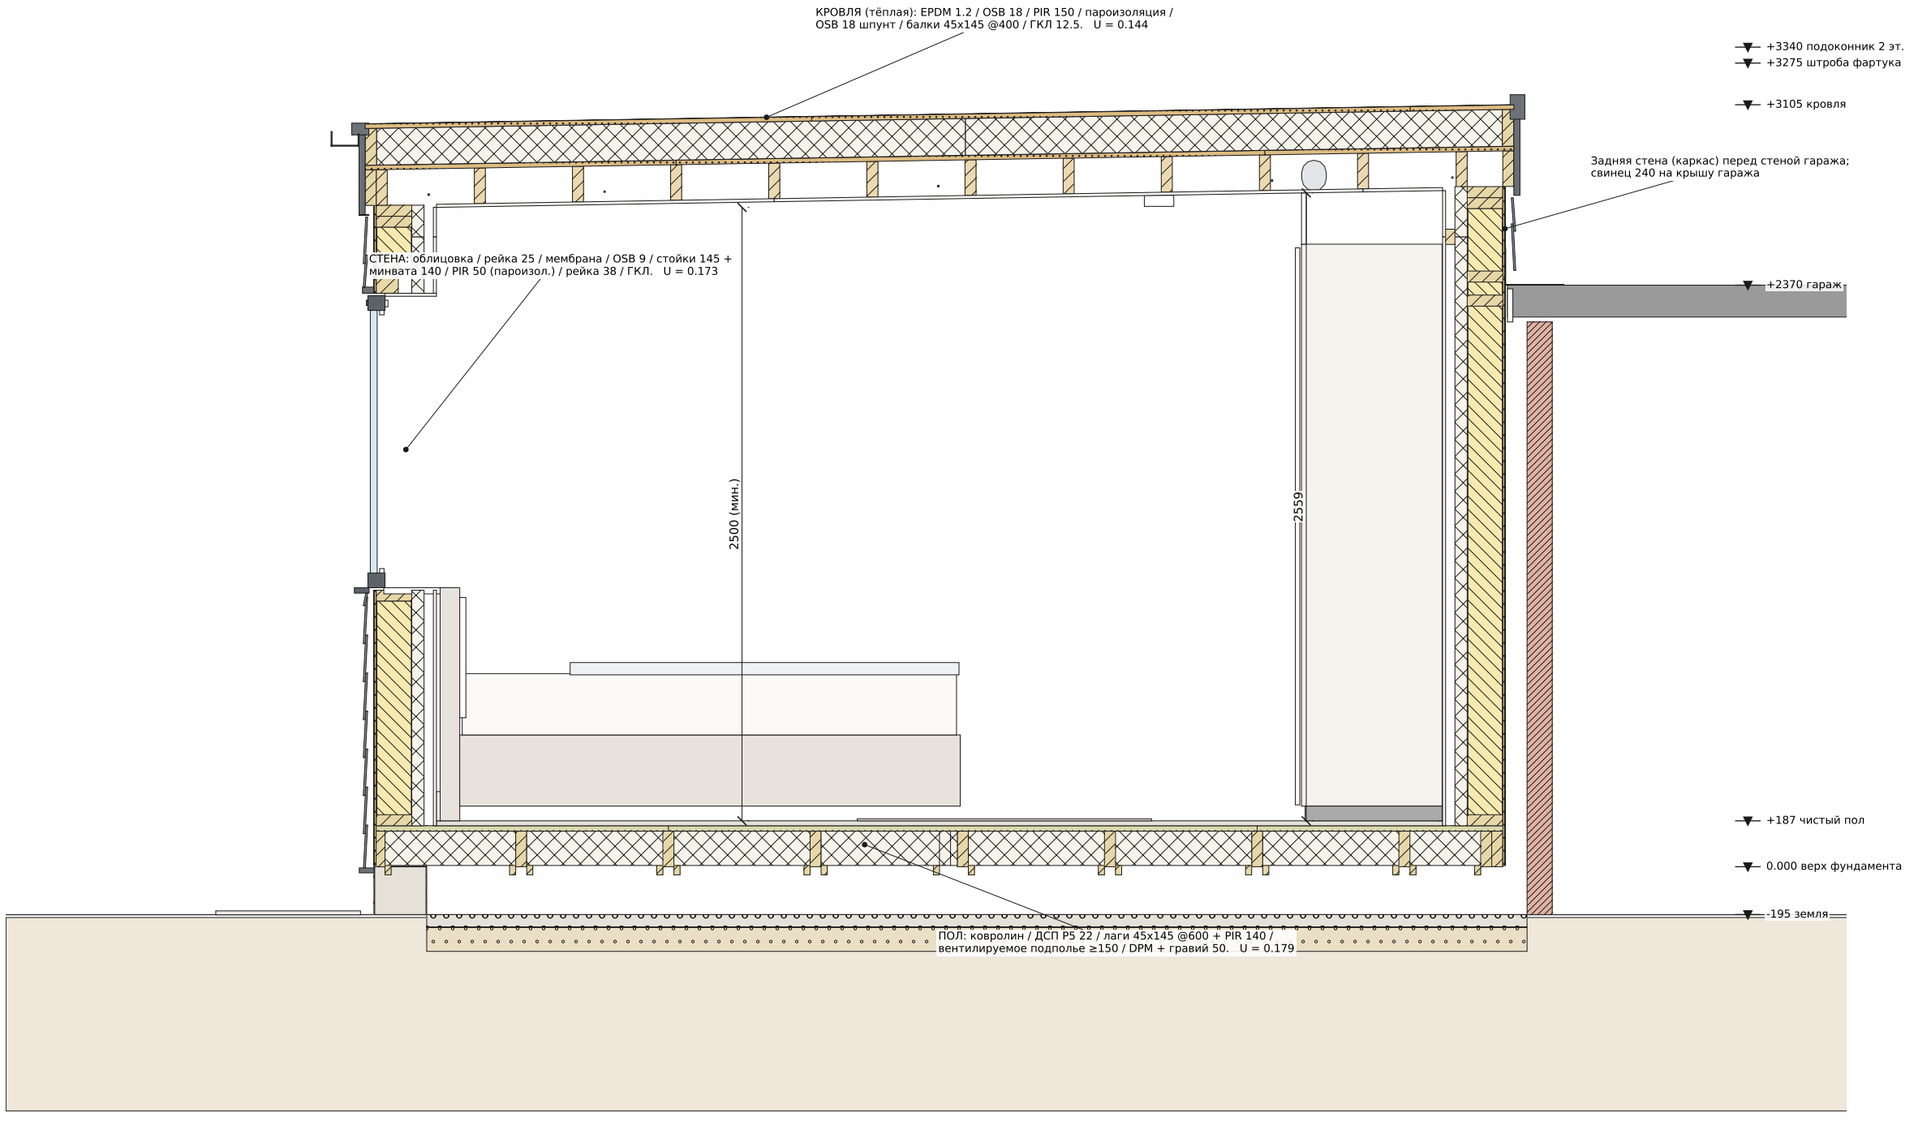


РАЗРЕЗ А-А (по оси окна, x = 1260)


Пристройка-спальня (каркасная), 2.95 x 4.70 м	
Разрез А-А (продольный)	**Лист 05**
Масштаб 1:25 (А3)	10.10.2026 rev A

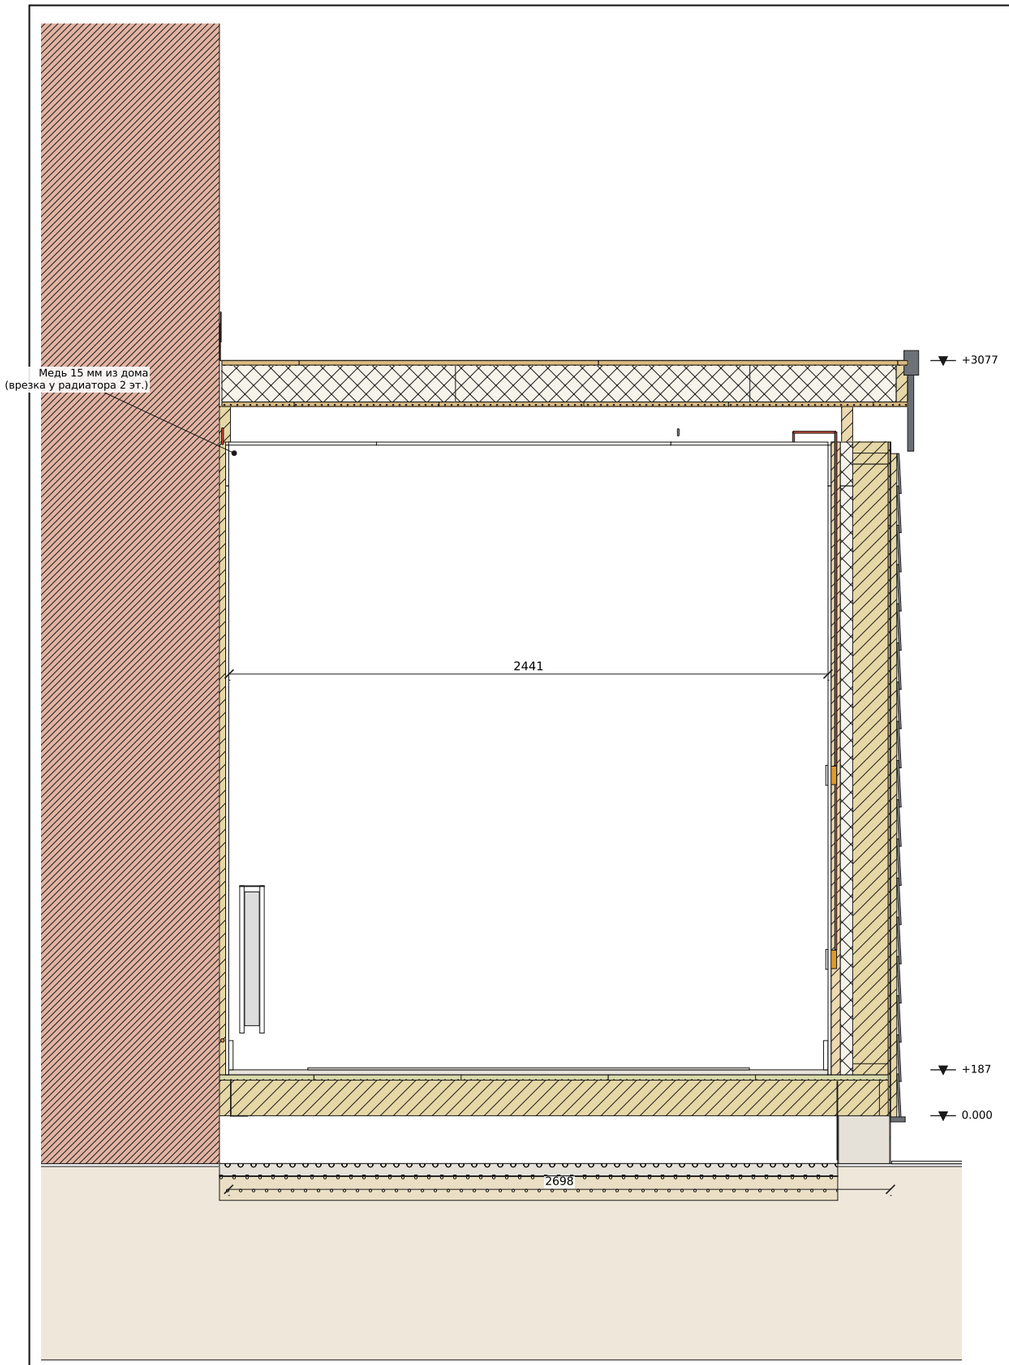


РАЗРЕЗ Б-Б (у = 3000)

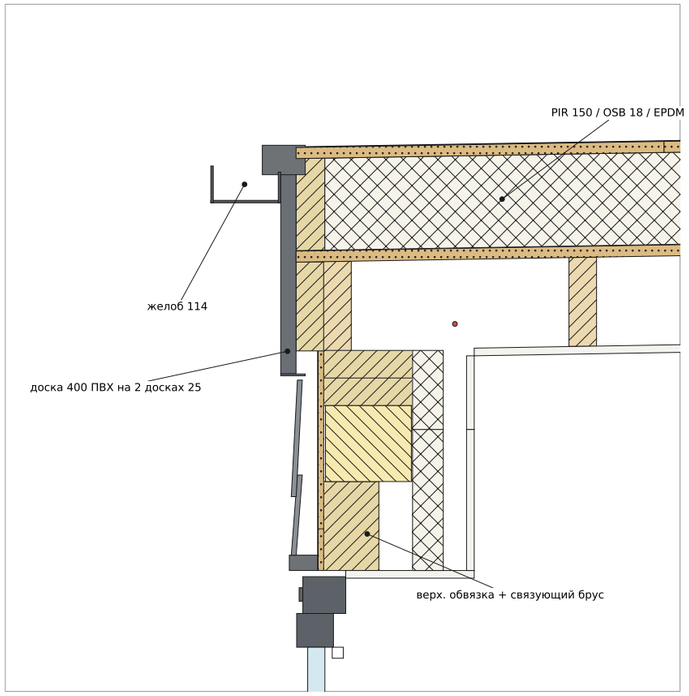


УЗЕЛ 2: карниз и желоб (1:10)

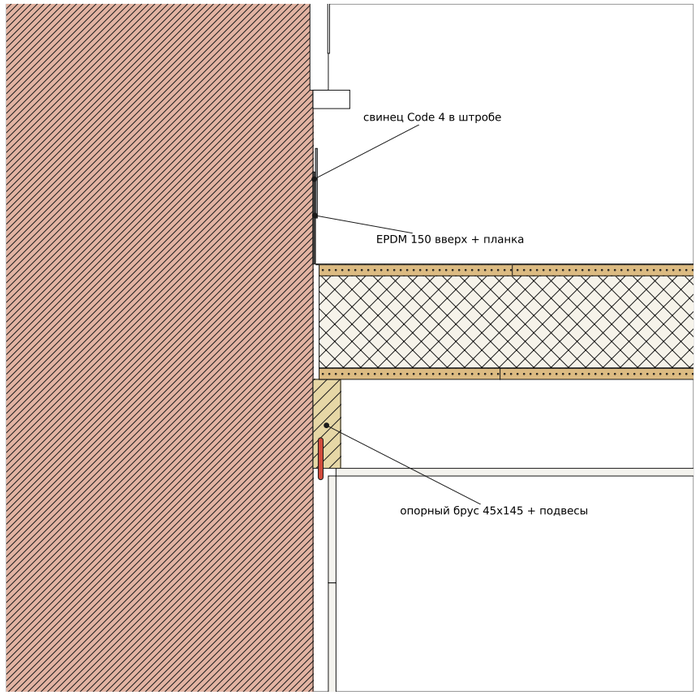


УЗЕЛ 3: примыкание к стене дома (1:10)

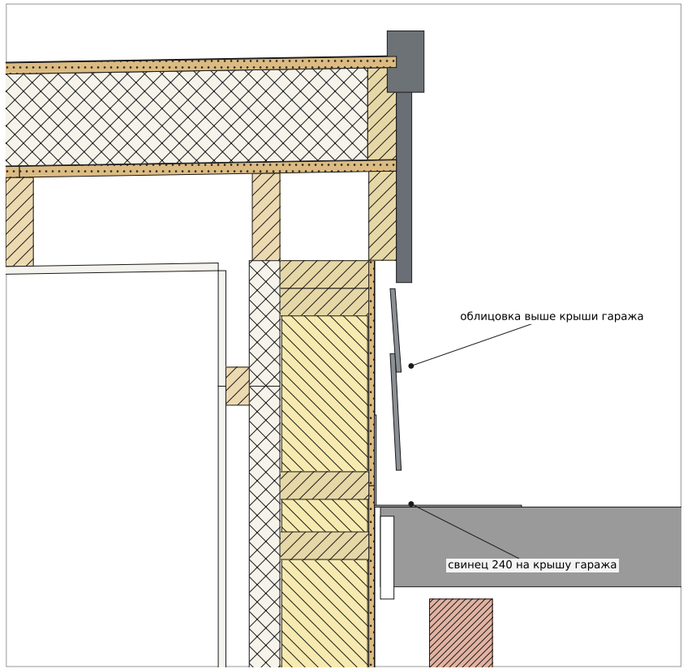


УЗЕЛ 4: задняя стена / крыша гаража (1:10)

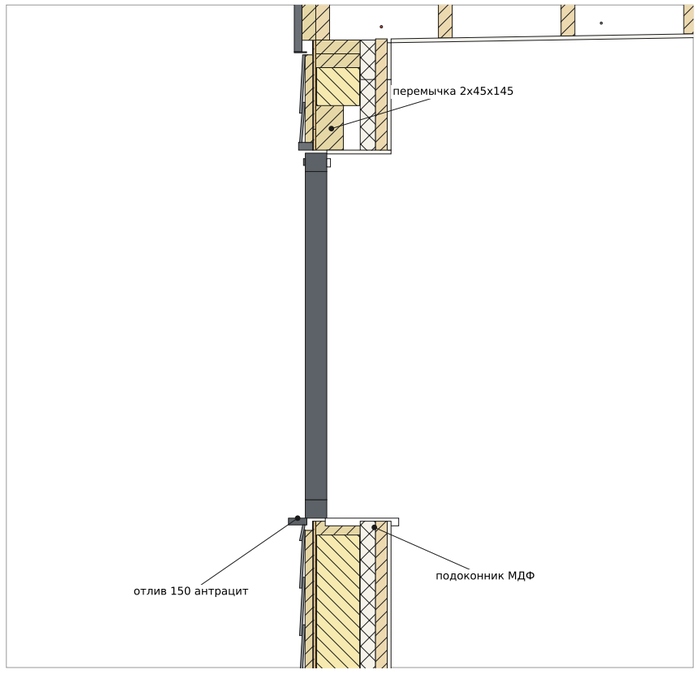


Пристройка-спальня (каркасная), 2.95 x 4.70 м	
Разрез Б-Б и узлы	**Лист 06**
Масштаб 1:25 / 1:10 (А3)	10.10.2026 rev A

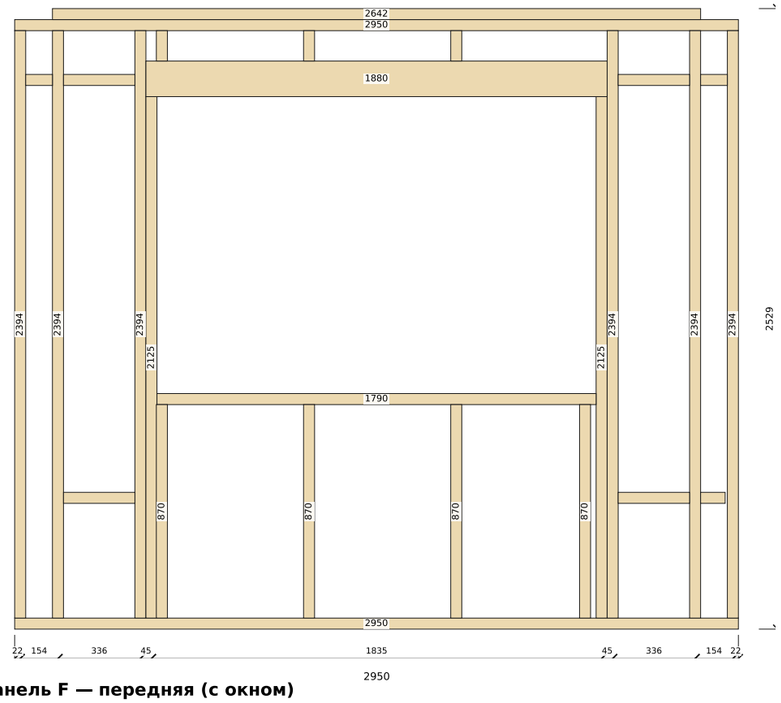


Панель F — передняя (с окном)

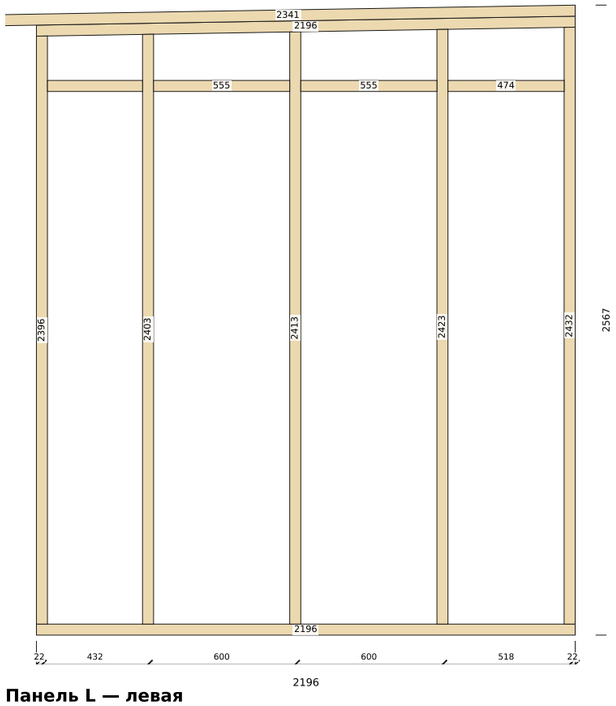


Панель L — левая

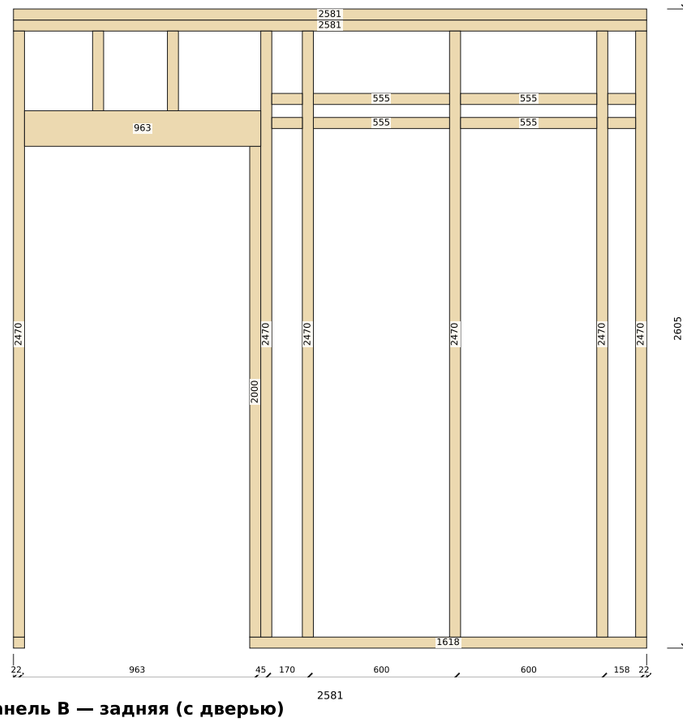

Панель B — задняя (с дверью)

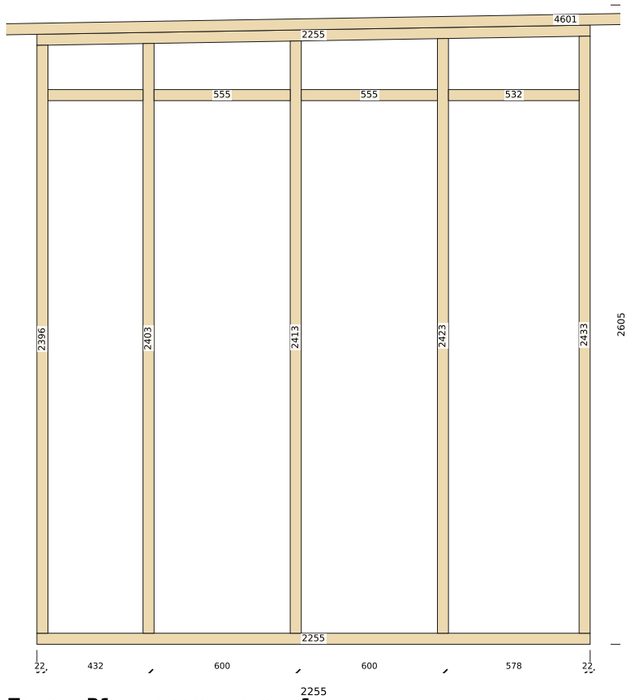

Панель R1 — правая, панель 1

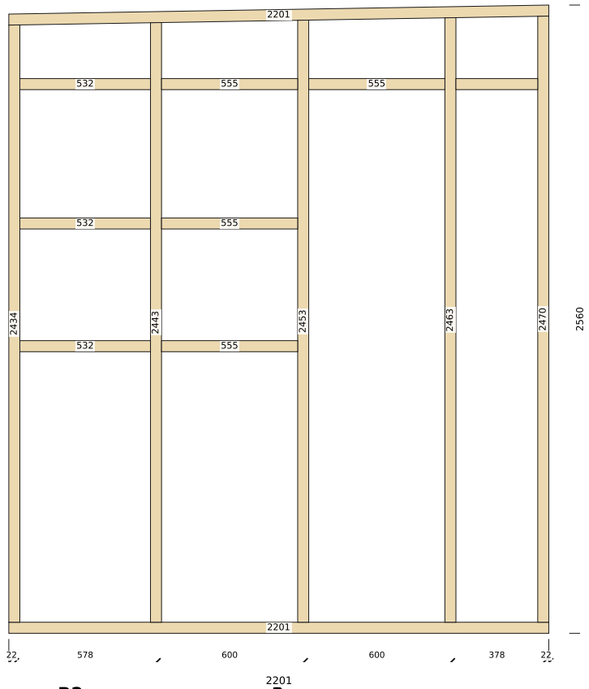


Панель R2 — правая, панель 2

ОБЩИЕ УКАЗАНИЯ ПО ПАНЕЛЯМ

- Собирать на ровном настиле пола, проверять диагонали (±3 мм).
- Нижняя обвязка + стойки + верхняя обвязка — гвозди 3.1x90 (2 на узел) или саморезы 5x100; связующий брус ставится после подъёма панелей.
- OSB 9 мм прибивать до подъёма: гвозди 2.8x50 ершёные @150 по краям, @300 в поле; зазор между листами 3 мм.
- Боковые стены L, R1, R2 имеют наклонный верх 1:60 — каждая стойка своей длины (цифры на схеме).
- Панели крепить к настилу/обвязке саморезами 6x150 @400, к дому — нерж. уголками + химанкер М10.
- Оконный проём: 1790 x 1210 (окно 1770x1190 + 10 мм по периметру).

Пристройка-спальня (каркасная), 2.95 x 4.70 м	
Стеновые панели: схемы каркаса (вид изнутри)	**Лист 07**
Масштаб 1:25 (А3). Размеры стоек — длина реза, мм.	10.10.2026 rev A

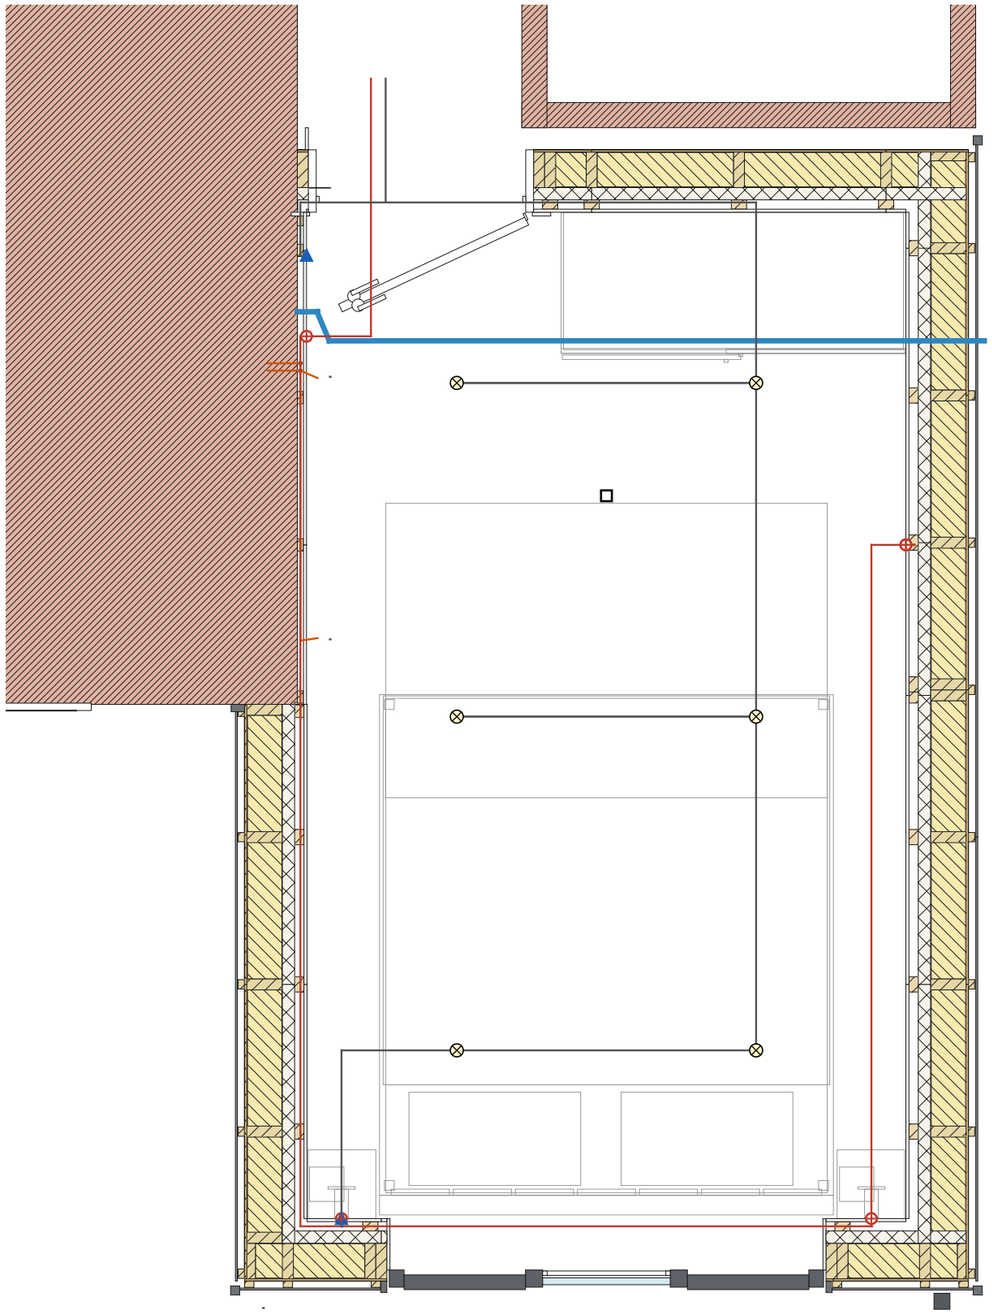

○+ розетка 13A двойная (2 с USB-C у кровати)

▲ выключатели: 2-кл. у входа (свет/улица), проходной у кровати

⊗ точечные LED 6 Вт (6 шт), диммер

□ датчик дыма сетевой, связанный (Part B)

— 4 мм² радиальная розеточная линия 32A (есть в проходе)

— 1.5/2.5 мм² освещение (2.5 есть в проходе)

— медь 15 мм отопление: подача/обратка

— воздуховод Ø100 вытяжки кухни (через потолок)

ЭЛЕКТРИКА (BS 7671, Part P)
• Кабели в монтажной зоне 38 мм за ГКЛ — вертикально/горизонтально от розеток (safe zones), через балки — отверстия по центру высоты (≥50 мм от краёв).
• Пароизоляцию (фольга PIR) не прорезать: подрозетники только в монтажной зоне.
• Розеточная линия 4 мм² — радиальная 32A с УЗО 30 мА; освещение 6A.
• Новые цепи/работы в пристройке уведомляемые: подключение, испытания и сертификат EIC — зарегистрированный электрик (NICEIC/NAPIT).

ОТОПЛЕНИЕ
• Врезка тройниками в подачу/обратку радиатора 2 этажа (под полом).
• Проход через стену на ≈+2700 в гильзах, опуск в облицовке стены дома (рейка 25) к радиатору 600x1000 тип 22 (≈1260 Вт при ΔT40).
• Теплопотери комнаты ≈557 Вт (−3/+20°C) — радиатор с запасом.
• После работ: промыть, долить ингибитор, развоздушить, балансировка.

ВЫТЯЖКА КУХНИ
• Существующий выход в стене дома (в плюще) — НЕ замуровывать.
• Жёсткий воздуховод Ø100 в коробе ГКЛ вверх, далее в межбалочном пространстве к правому фронтону, решётка с обратным клапаном.
• Убедиться, что это не дымоход котла (иначе — только через Gas Safe).

ПЛАН ЭЛЕКТРИКИ И ОТОПЛЕНИЯ

Пристройка-спальня (каркасная), 2.95 x 4.70 м	
Инженерные сети: электрика, отопление, вытяжка	**Лист 08**
Масштаб 1:25 (A3)	10.10.2026 rev A